

FOND DE PLAN :

TECTONIKES, Architectes Niveau RdC Réf : 05155-EXE-RDC-IND D du 23/04/2010

Figuration du fond de plan non contractuelle ; état du projet à la date référencée ci-dessus

Plan d'identification des lots de copropriété
« Les Symphonies » à SAINT-PRIEST

ZAC Mozart (Secteur 2)
VOLUME 4 - Rez-de-chaussée



LEGENDE :

Parties Communes

0 1 5 10
en mètres

Echelle 1/200 200942220-A-1-01 Avril 2010

Operandi
anc. Charmasson
CABINET DE GEOMETRES-EXPERTS



FOND DE PLAN :


TECTONIKES, Architectes Niveau 1er étage Réf : 05155-EXE-N01-IND B du 10/02/2010

Figuration du fond de plan non contractuelle ; état du projet à la date référencée ci-dessus

Servitude de passage de gaine particulière
au "commerce 04" jusqu'en toiture
(fonds servant : volume 4 ; fonds dominant : volume 3)

Plan d'identification des lots de copropriété « Les Symphonies » à SAINT-PRIEST

ZAC Mozart (Secteur 2)
VOLUME 4 - 1er Etage

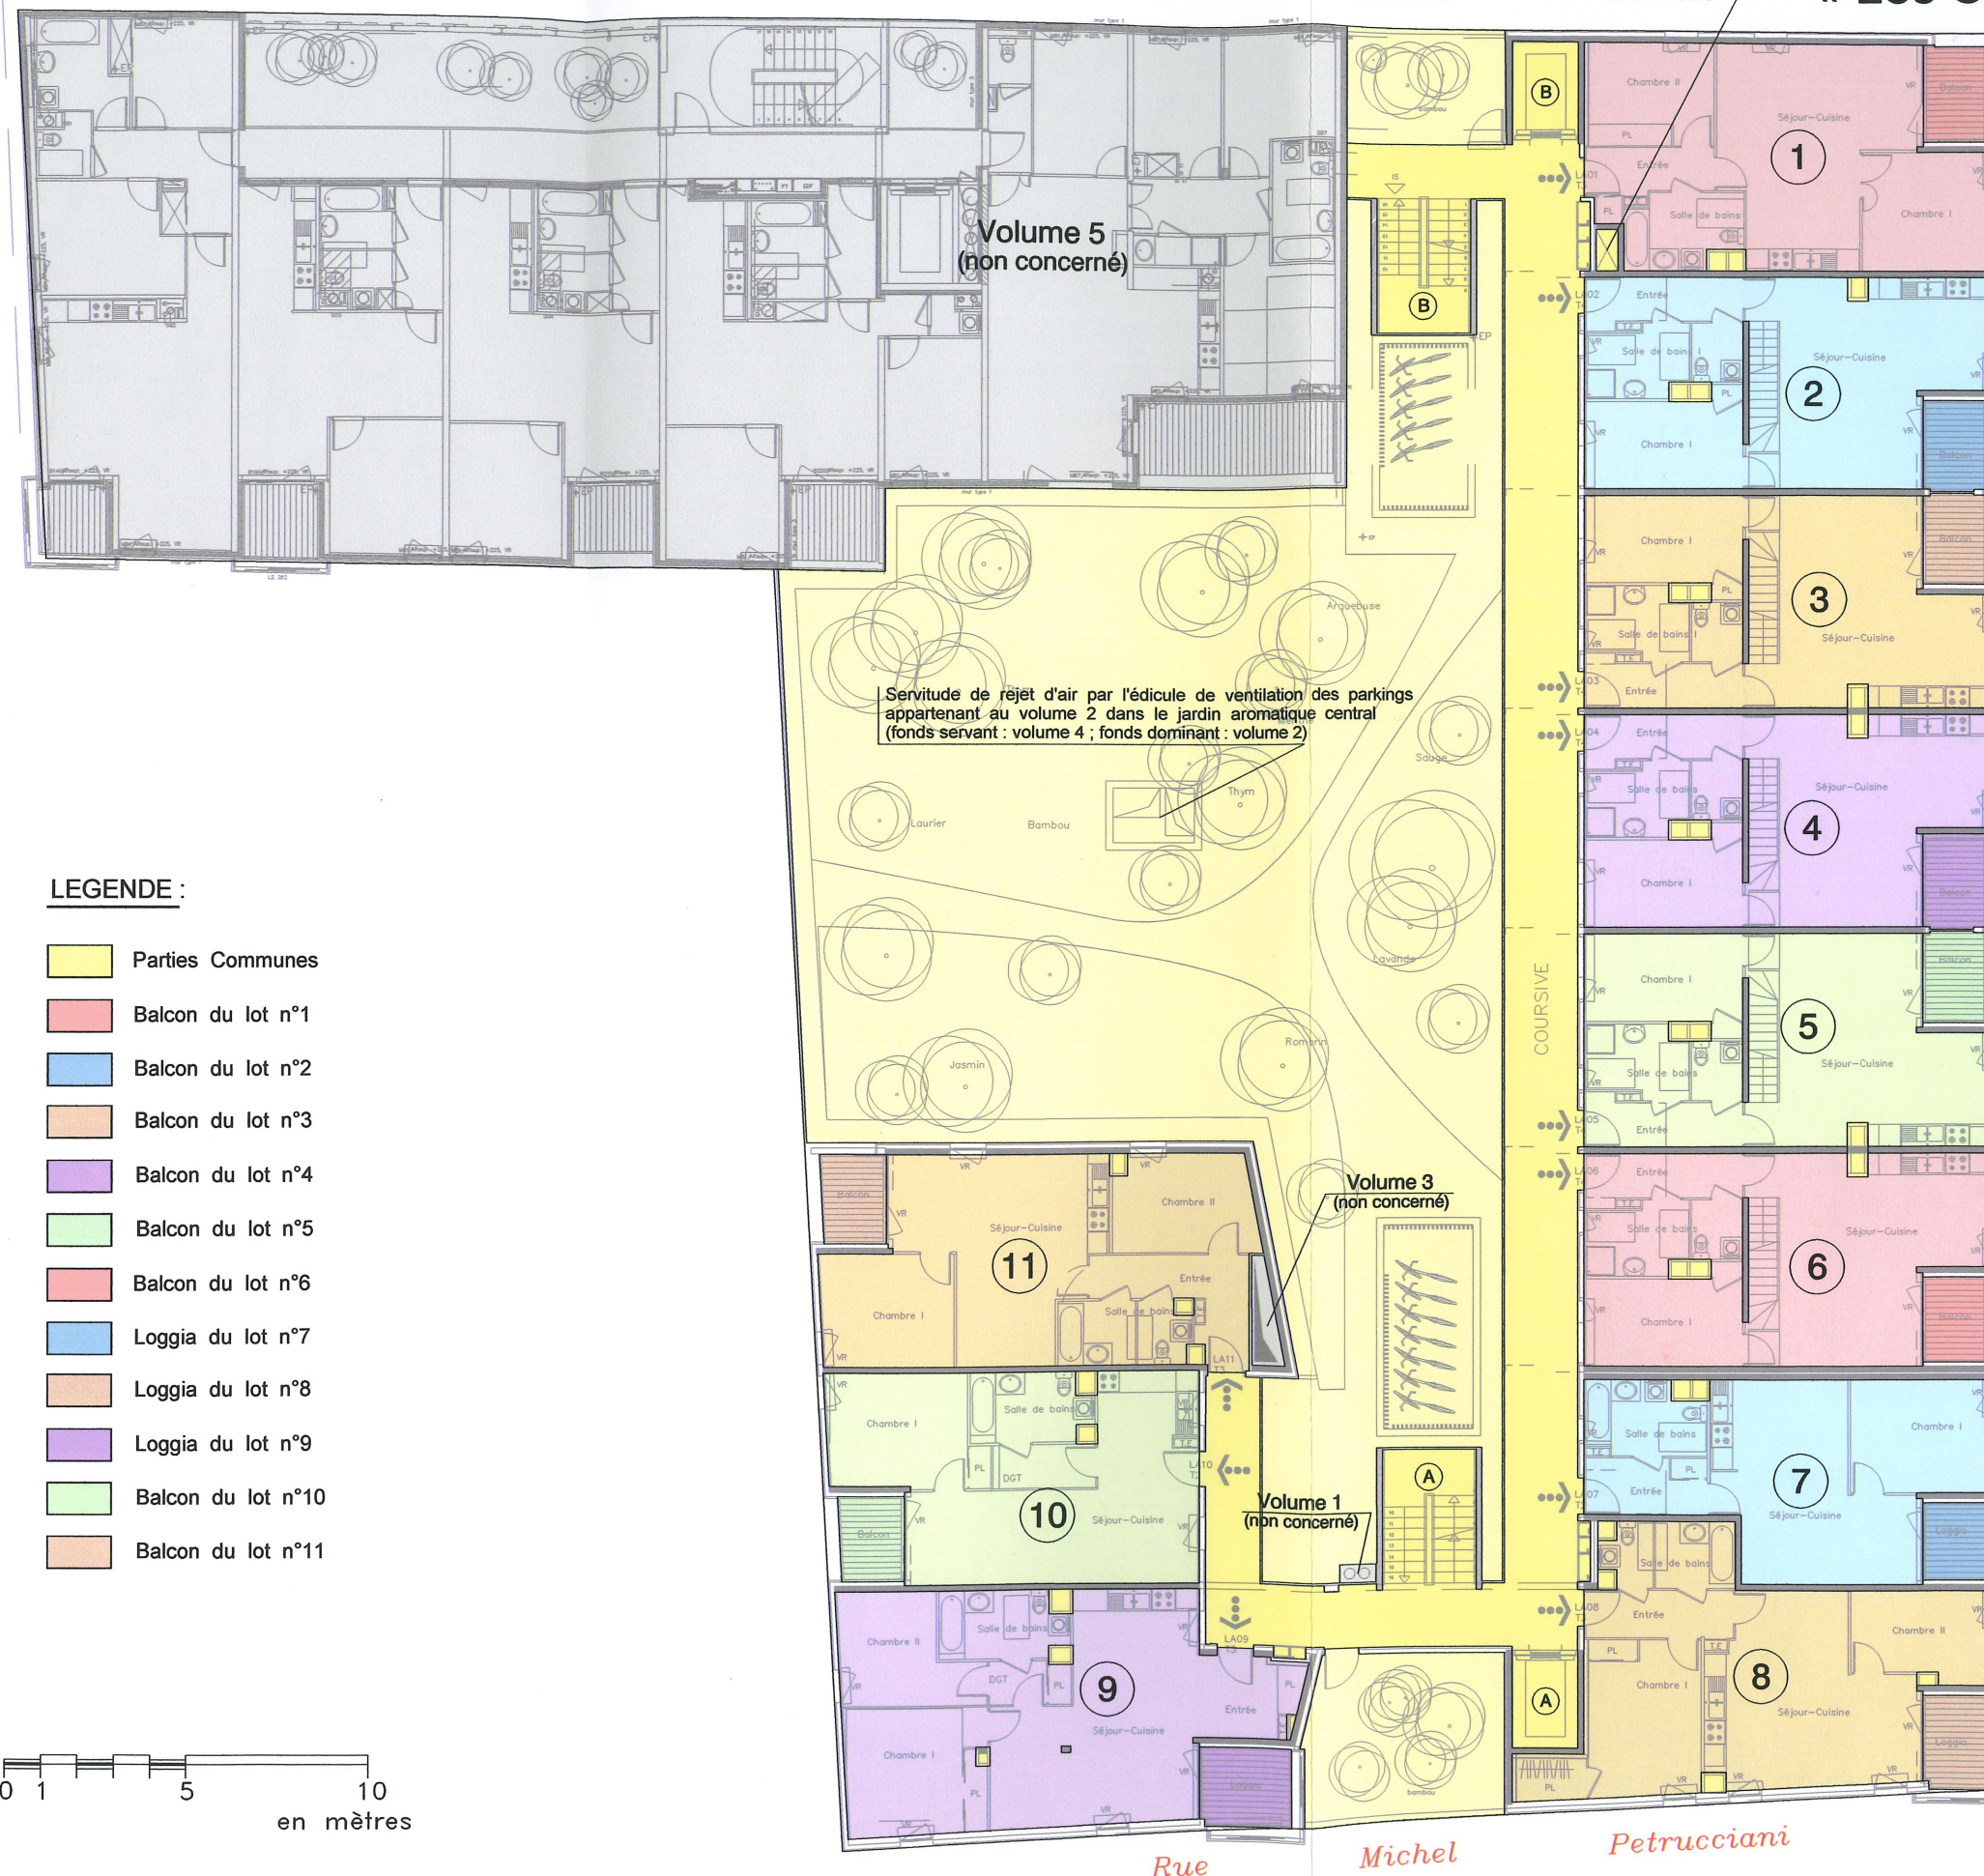

Operandi
anc. Charmasson
CABINET DE GEOMETRES-EXPERTS





Echelle 1/200 200942220-A-1-02 Avril 2010

FOND DE PLAN :

TECTONIKES, Architectes Niveau 2ème étage Réf : 05155-EXE-N02-IND B du 10/02/2010
Figuration du fond de plan non contractuelle ; état du projet à la date référencée ci-dessus


Plan d'identification des lots de copropriété « Les Symphonies » à SAINT-PRIEST

ZAC Mozart (Secteur 2)
VOLUME 4 - 2ème Etage

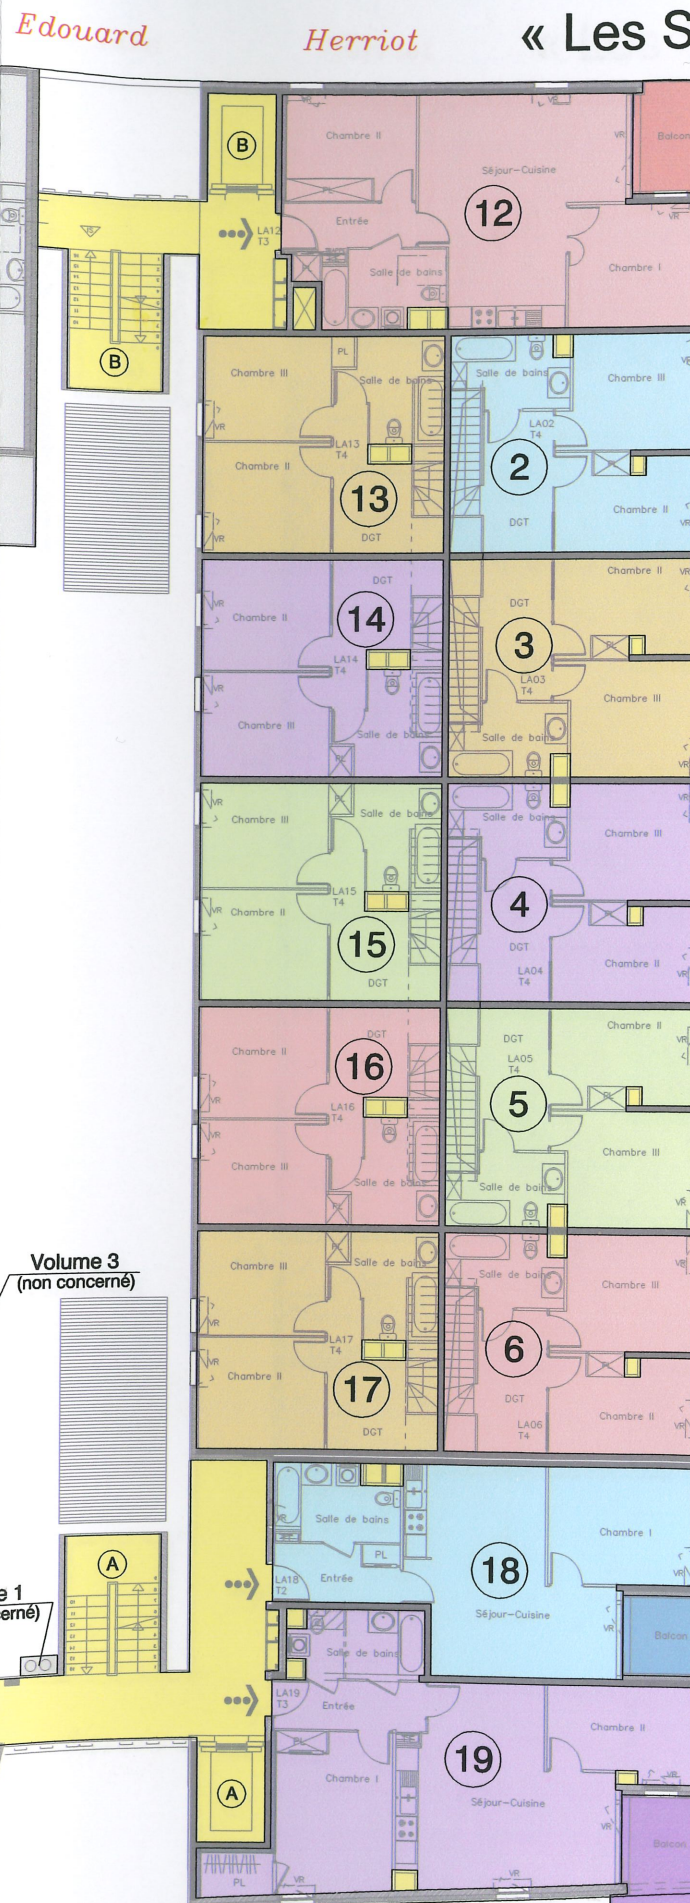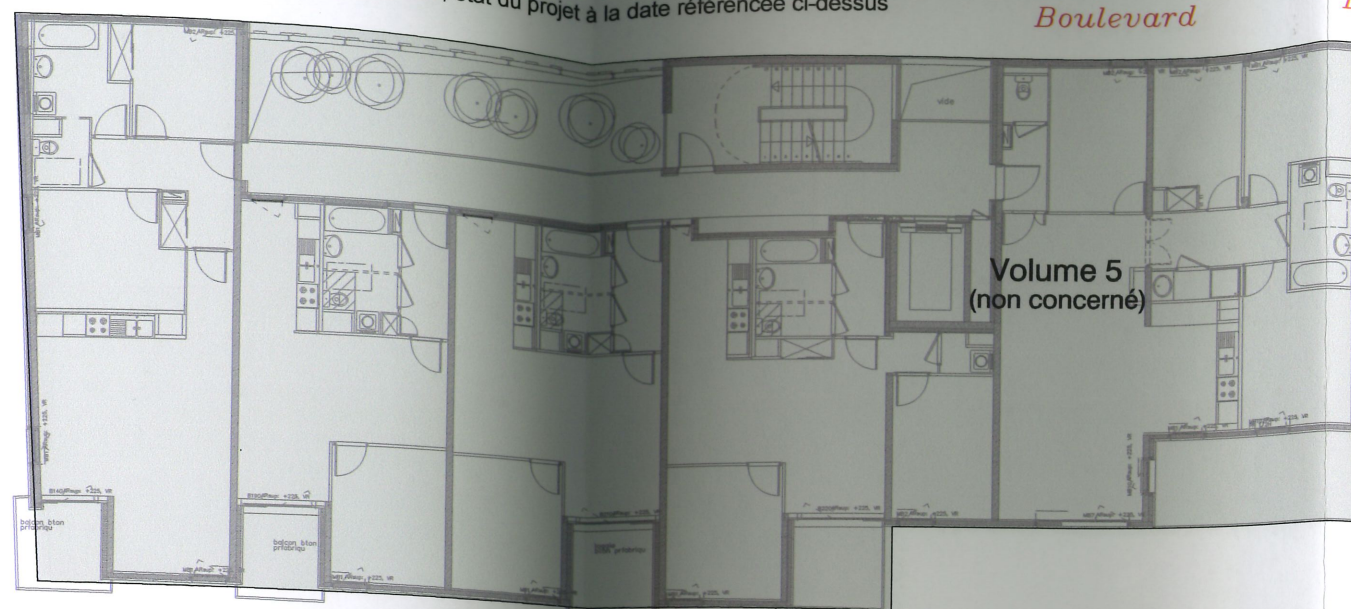

LEGENDE :

- Parties Communes
- Balcon du lot n°12
- Balcon du lot n°18
- Balcon du lot n°19
- Balcon du lot n°20
- Balcon du lot n°21
- Loggia du lot n°22

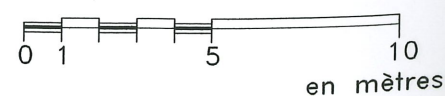

Operandi
anc. Charmasson
CABINET DE GEOMETRES-EXPERTS



Echelle 1/200 200942220-A-1-03 Avril 2010


FOND DE PLAN :

TECTONIKES, Architectes Niveau 3ème étage Réf : 05155-EXE-N03-IND B du 10/02/2010
Figuration du fond de plan non contractuelle ; état du projet à la date référencée ci-dessus

Plan d'identification des lots de copropriété

« Les Symphonies » à SAINT-PRIEST

ZAC Mozart (Secteur 2)
VOLUME 4 - 3ème Etage

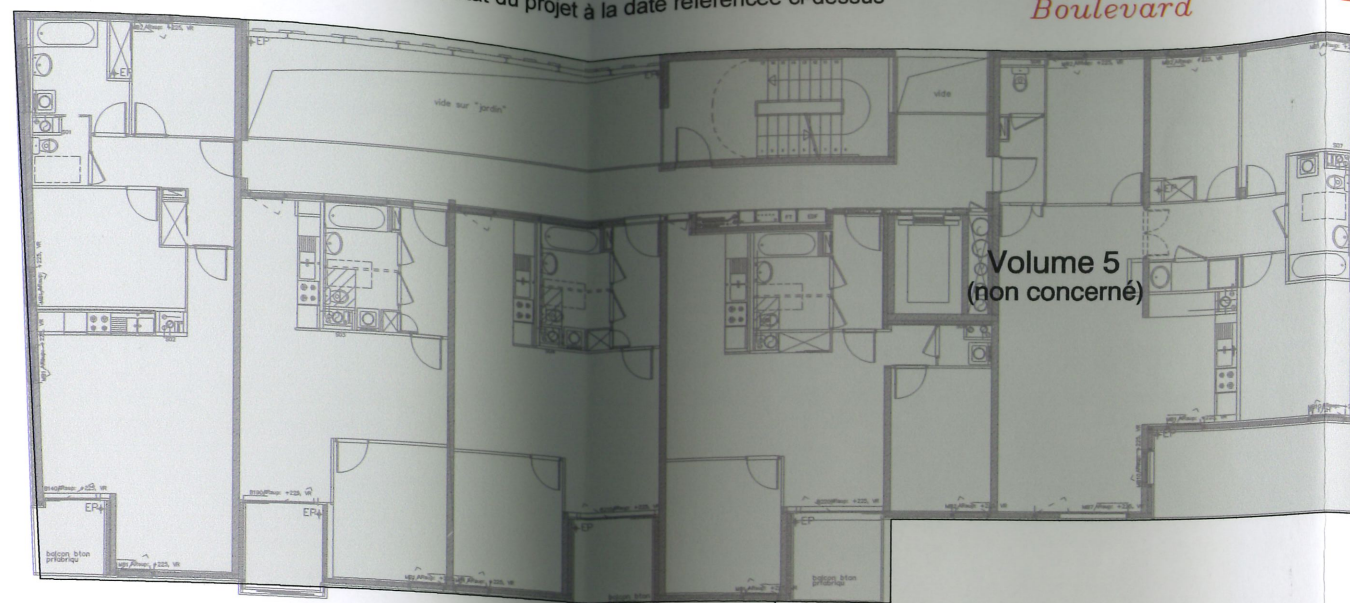



Edouard

Herriot

Boulevard

LEGENDE :

- Parties Communes
- Balcon du lot n°13
- Balcon du lot n°14
- Balcon du lot n°15
- Loggia du lot n°16
- Loggia du lot n°17
- Loggia du lot n°23
- Balcon du lot n°24
- Balcon du lot n°25
- Loggia du lot n°26
- Loggia du lot n°27
- Balcon du lot n°28

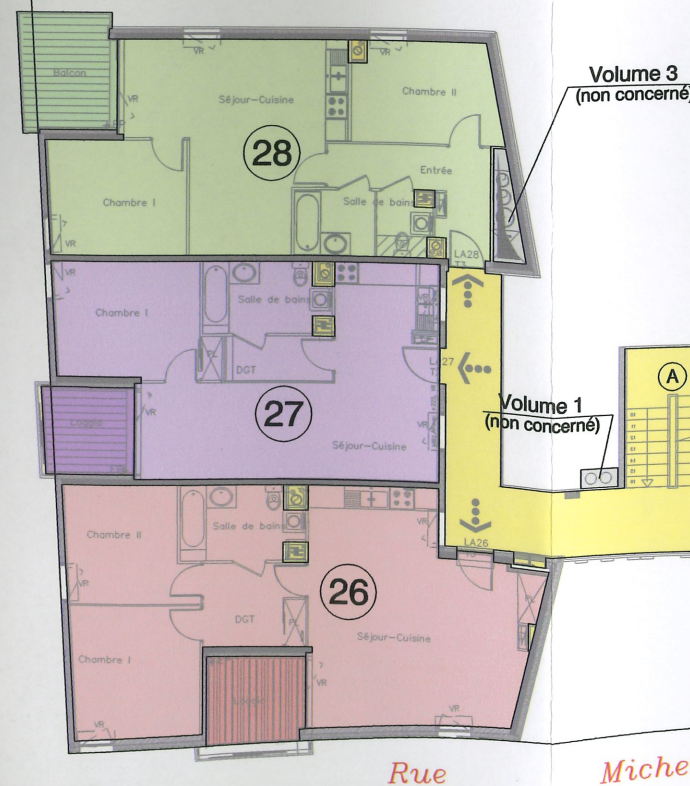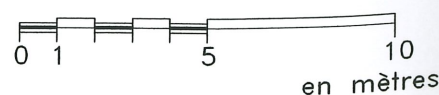

Michel

Petruciani

Rue

COURSIVE

Maréchal

Esplanade



Operandi
anc. Charmasson
CABINET DE GEOMETRES-EXPERTS



Echelle 1/200 200942220-A-1-04 Avril 2010


FOND DE PLAN :

TECTONIKES, Architectes Niveau 4ème étage Réf : 05155-EXE-N04-IND B du 10/02/2010
Figuration du fond de plan non contractuelle ; état du projet à la date référencée ci-dessus

Plan d'identification des lots de copropriété

« Les Symphonies » à SAINT-PRIEST


ZAC Mozart (Secteur 2)
VOLUME 4 - 4ème Etage

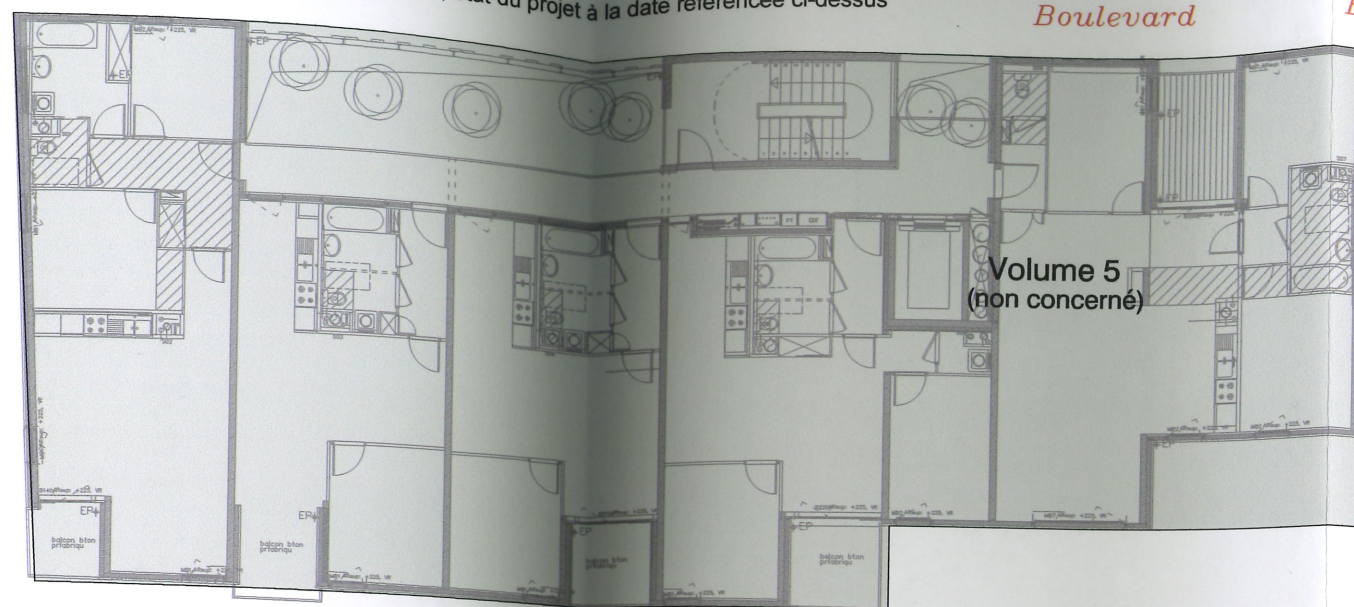

LEGENDE :

- Parties Communes
- Balcon du lot n°29
- Balcon du lot n°30
- Balcon du lot n°31
- Balcon du lot n°32
- Balcon du lot n°33
- Balcon du lot n°34
- Balcon du lot n°35
- Balcon du lot n°36
- Loggia du lot n°37
- Balcon du lot n°38
- Balcon du lot n°39

0 1 5 10
en mètres

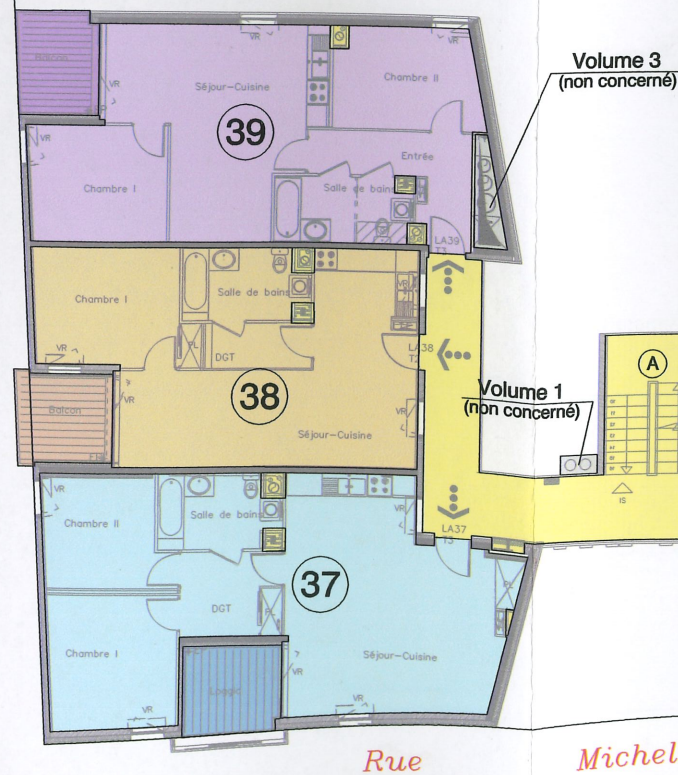

Edouard

Herriot

COURSIÈRE

Maréchal

Esplanade



Michel

Petruciani

Rue

Operandi
anc. Charmasson
CABINET DE GEOMETRES-EXPERTS



Echelle 1/200 200942220-A-1-05 Avril 2010


FOND DE PLAN :

TECTONIKUES, Architectes Niveau 5ème étage Réf : 05155-EXE-N05-IND B du 10/02/2010
Figuration du fond de plan non contractuelle ; état du projet à la date référencée ci-dessus


Plan d'identification des lots de copropriété

« Les Symphonies » à SAINT-PRIEST

ZAC Mozart (Secteur 2)
VOLUME 4 - 5ème Etage

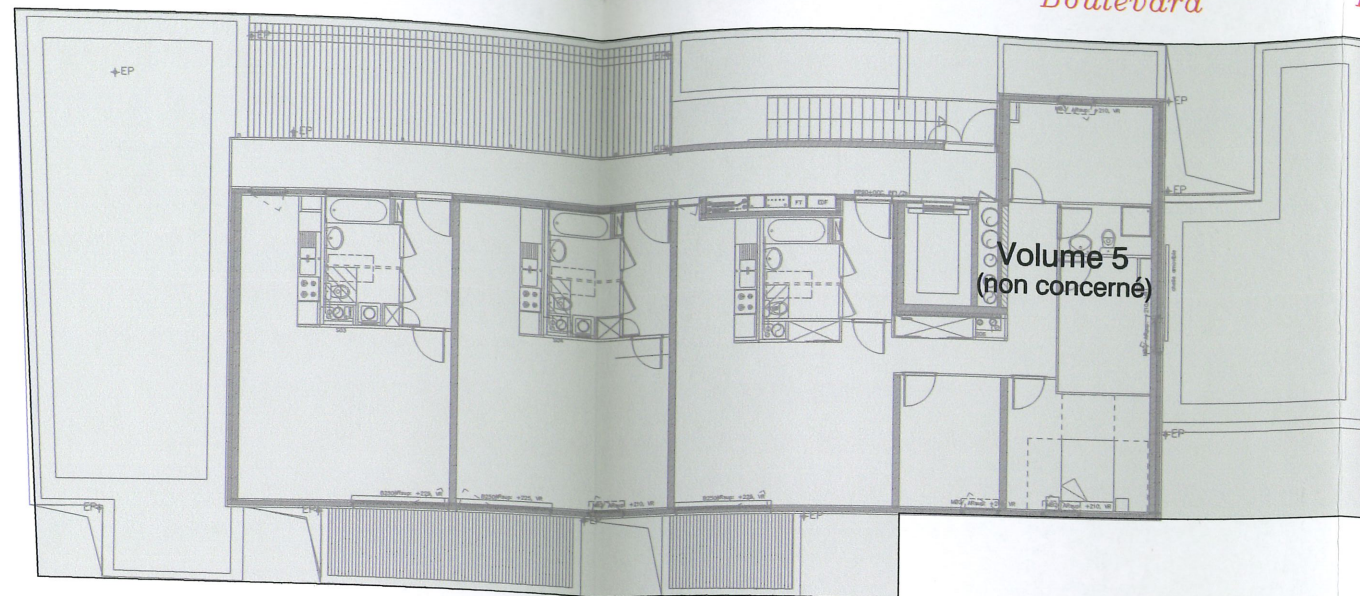

Volume 5
(non concerné)

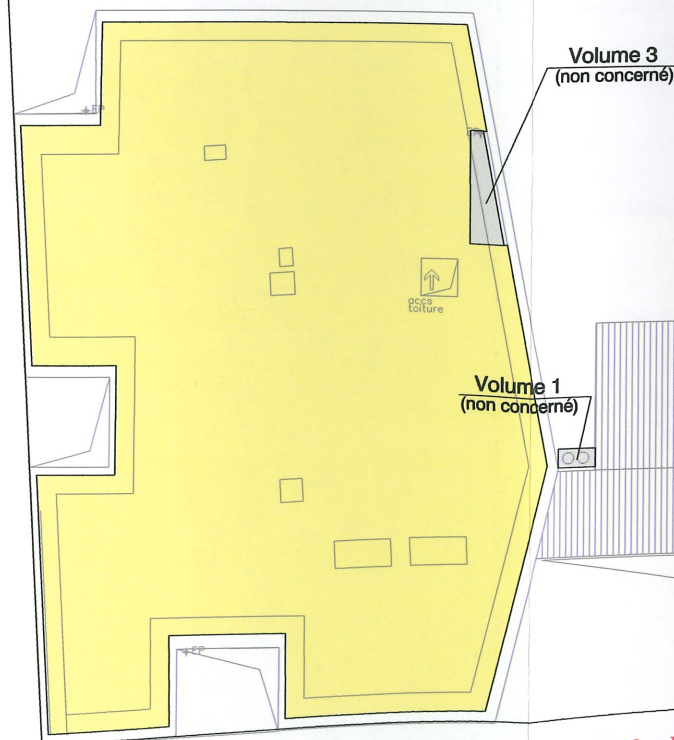


Volume 3
(non concerné)

Volume 1
(non concerné)

LEGENDE :

Parties Communes

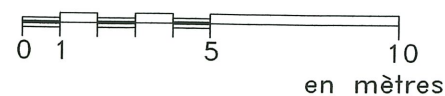

Boulevard

Edouard

Herriot

Maréchal

Esplanade

Rue

Michel

Petruciani



Operandi
anc. Charmasson
CABINET DE GEOMETRES-EXPERTS



Echelle 1/200 200942220-A-1-06 Avril 2010