


80 Koléroue, 2cm.

Lotissement "Le Dauphin II"

Commune de Charvieu Chavagneux

Plan d'Ensemble

Echelle : 1/1000

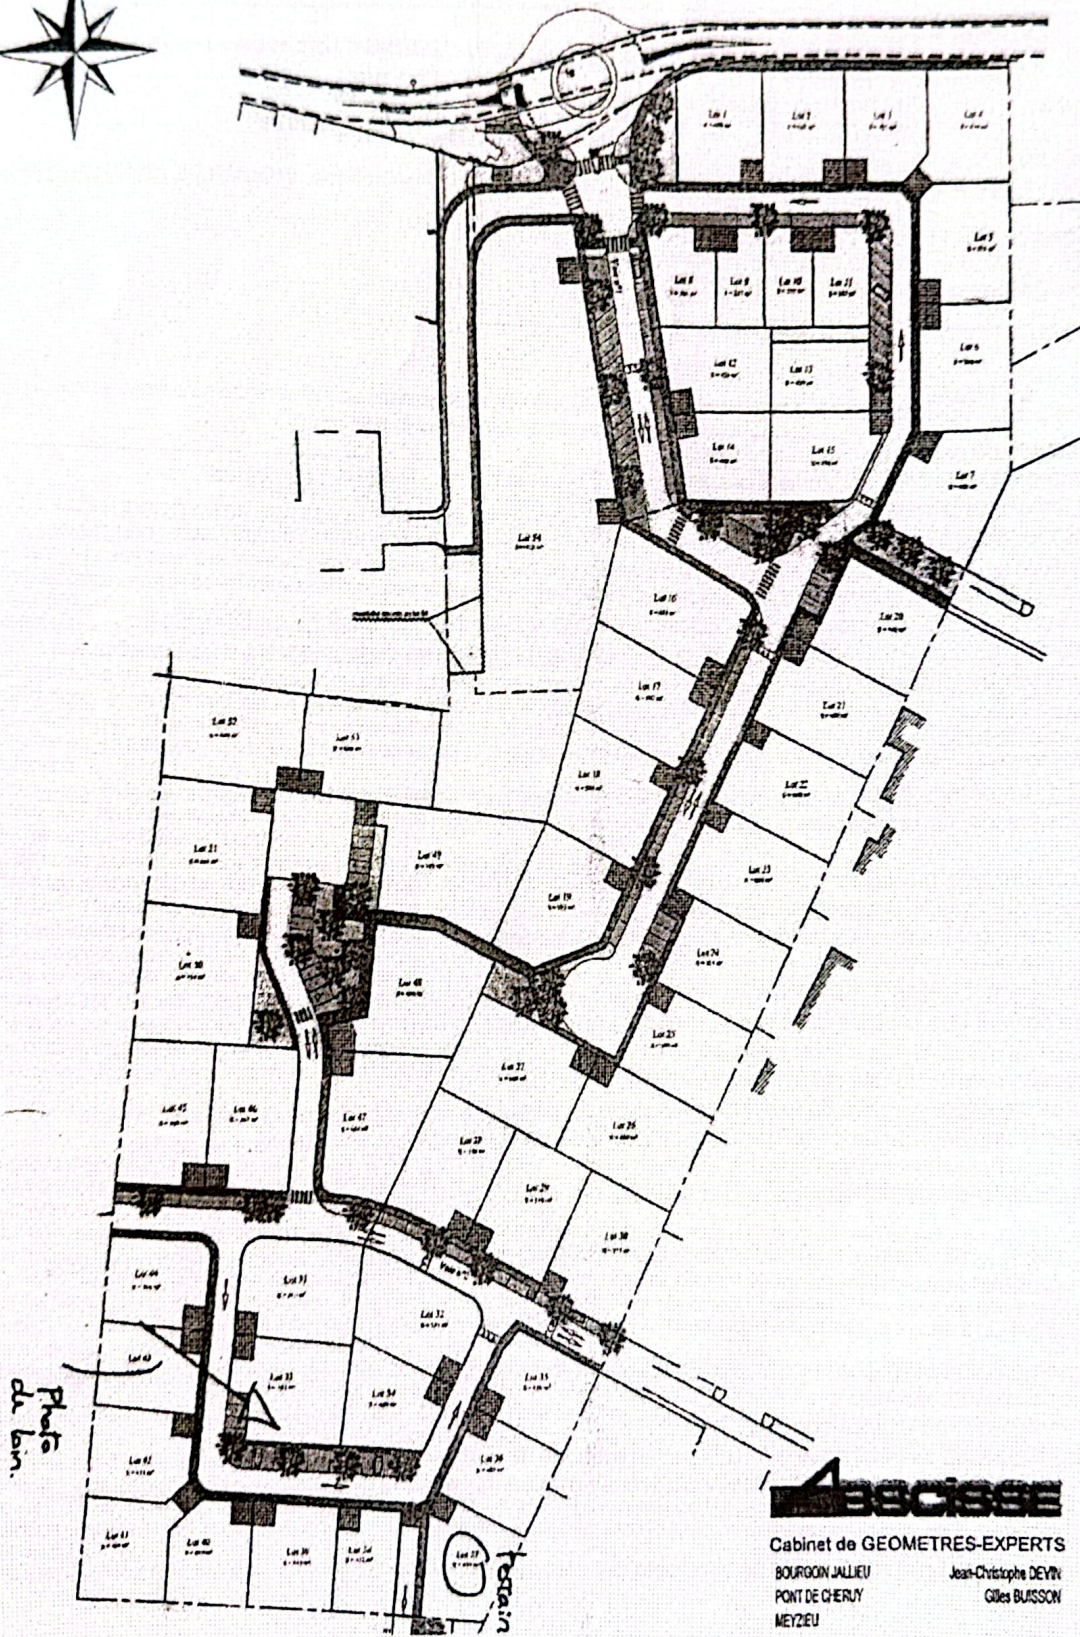


ABSCISSE

Cabinet de GEOMETRES-EXPERTS
BOURGOIN JALLIEU
PONT DE CHERY
MEYZIEU

Jean-Christophe DEVIN
Gilles BUSSON

PC 717

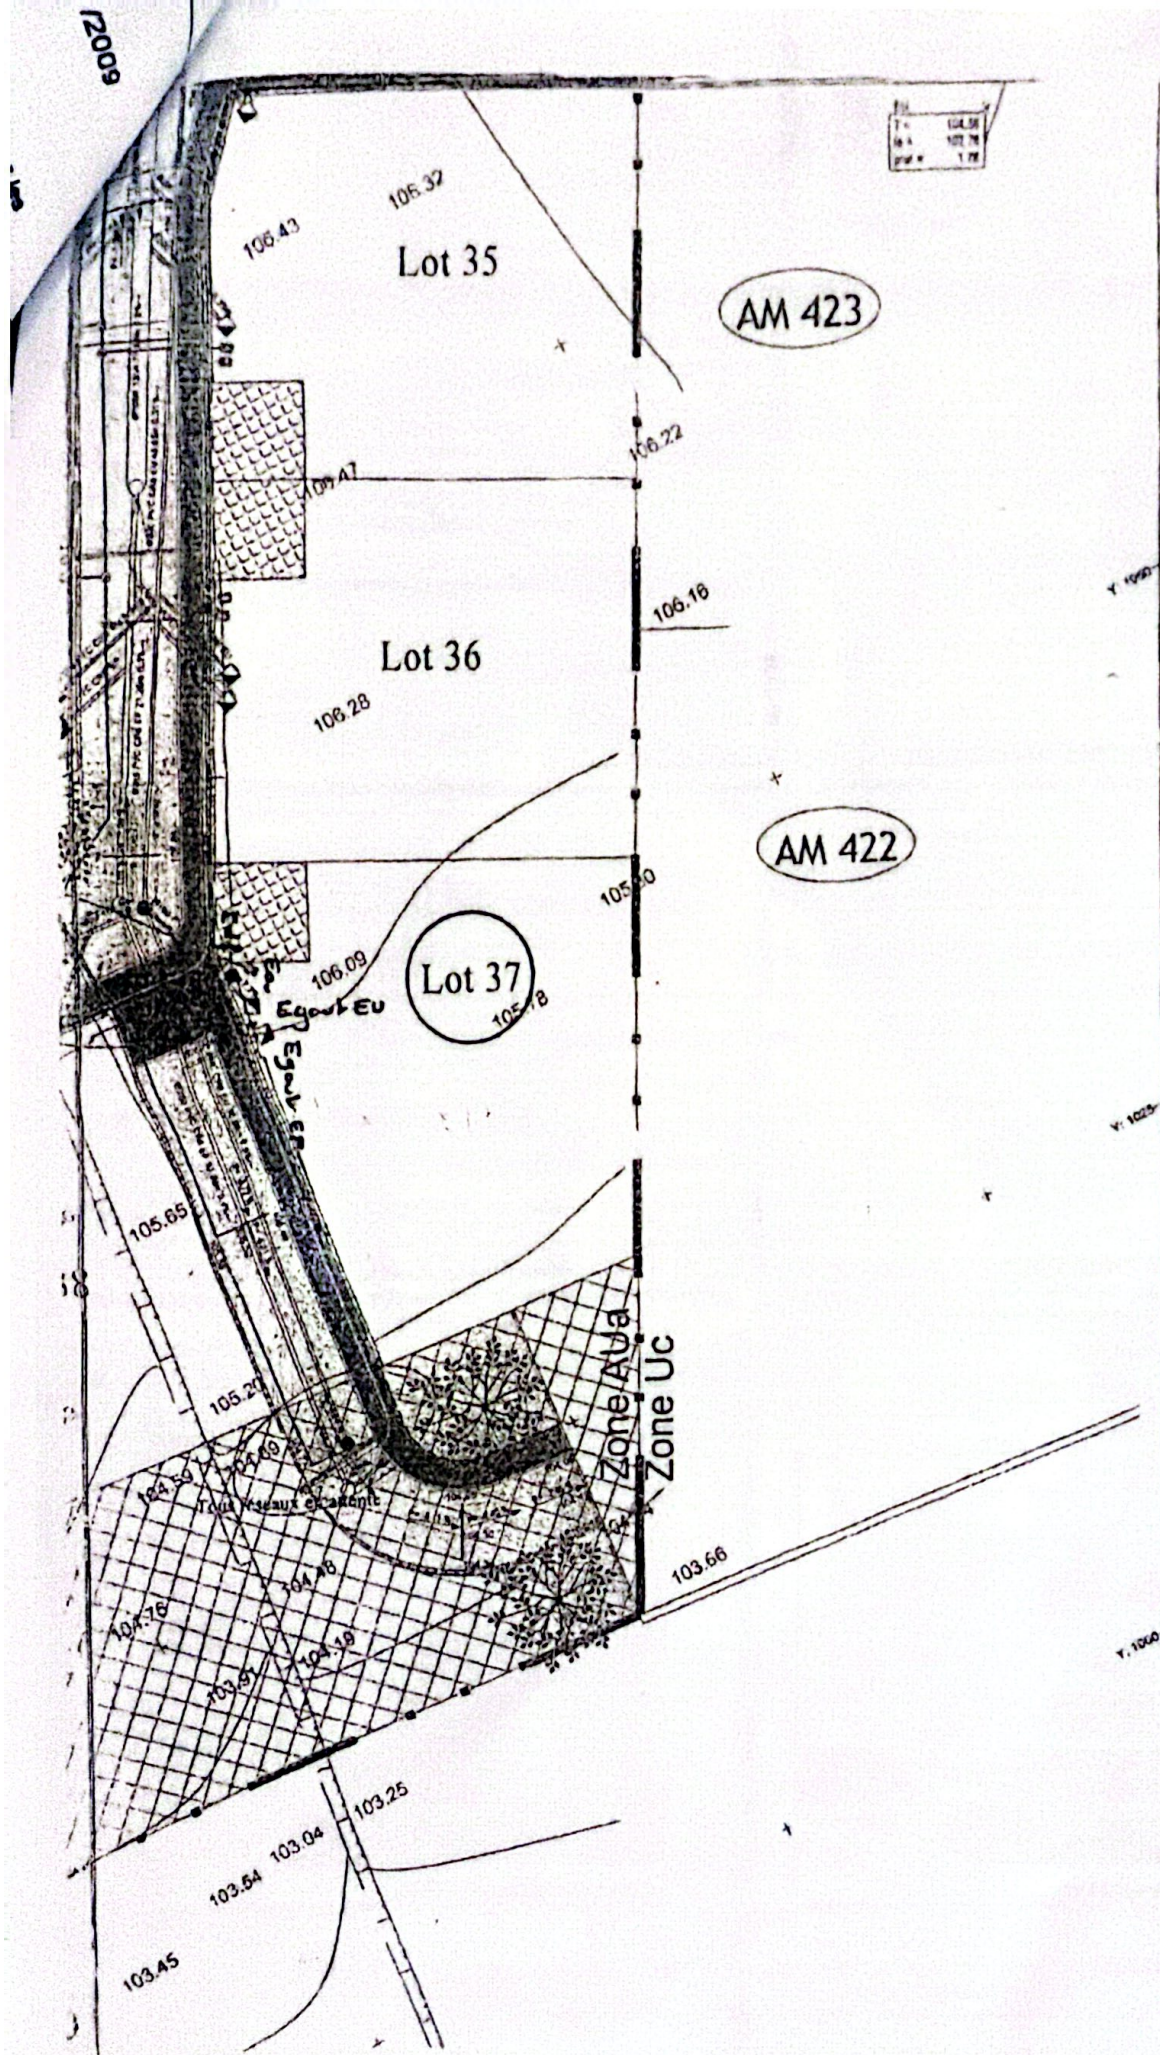

Réseaux

PC 011